


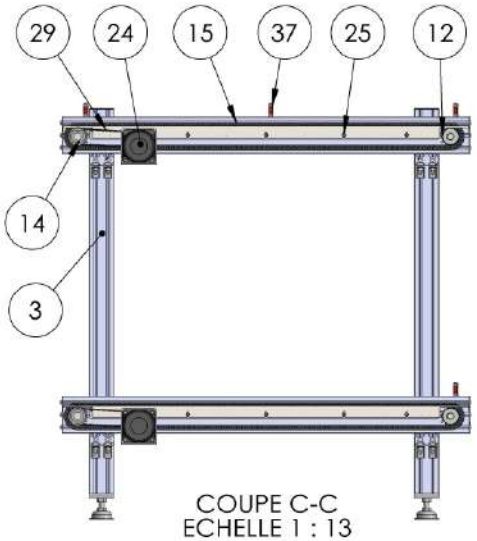


COUPE C-C
ECHELLE 1 : 13

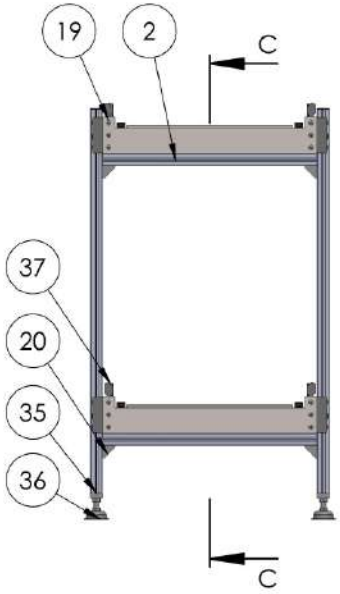


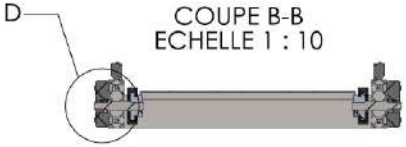


COUPE B-B
ECHELLE 1 : 10

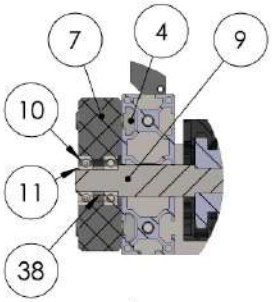


DÉTAIL D
ECHELLE 1 : 3

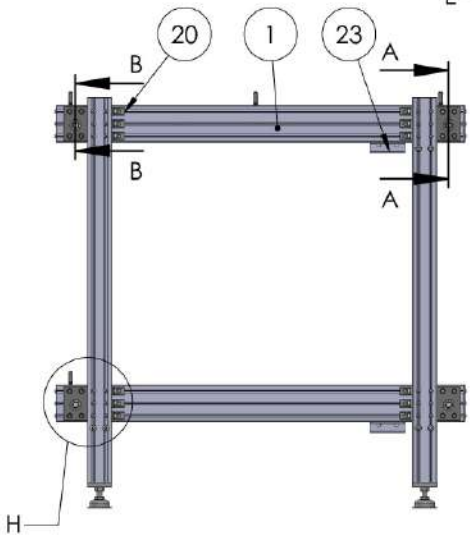


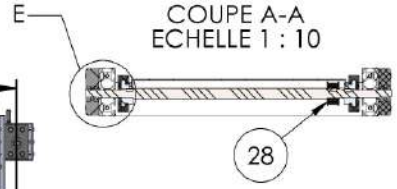


COUPE A-A
ECHELLE 1 : 10

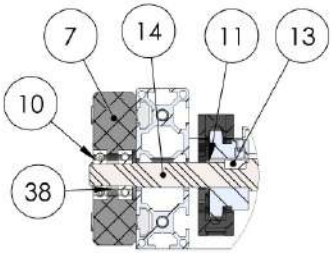



DÉTAIL E
ECHELLE 1 : 3

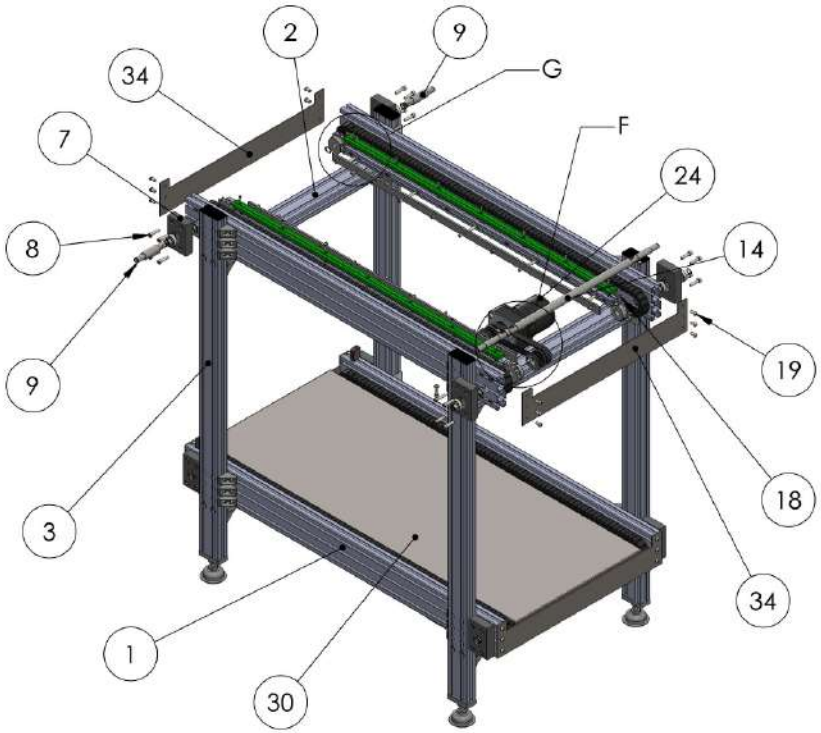

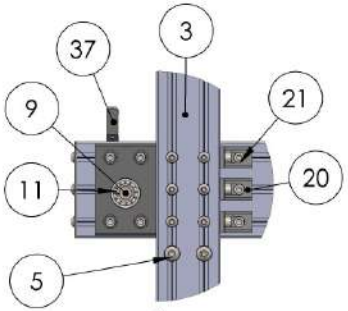


DÉTAIL H
ECHELLE 1 : 5

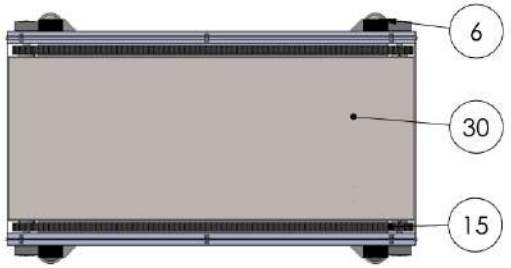

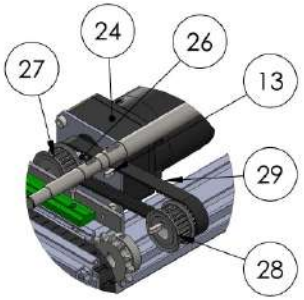



DÉTAIL F
ECHELLE 1 : 5

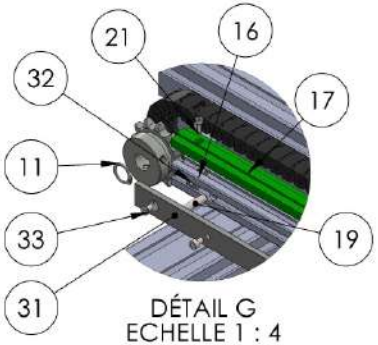


DÉTAIL G
ECHELLE 1 : 4

Ecole Nationale d'Ingénieurs de Bizerte			
Echelle : 1:13	**Convoyeur à deux étages**		Document 1
			Dessiné par: Hamdi.A
A3	© Ahmed Hamdi	Société: [redacted]	Page 1/2

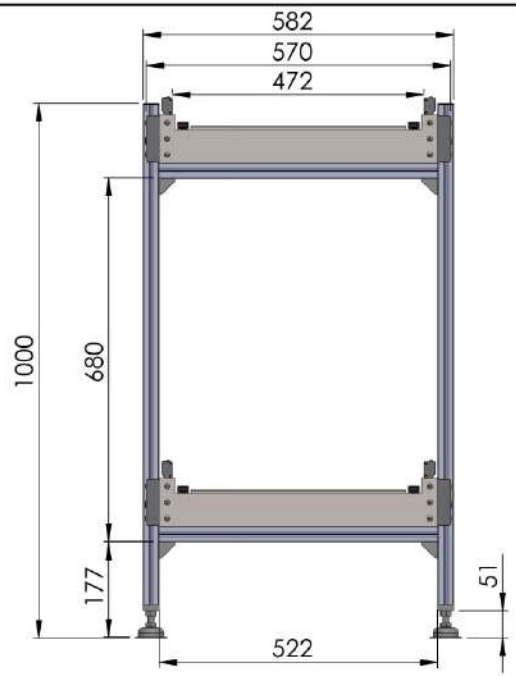


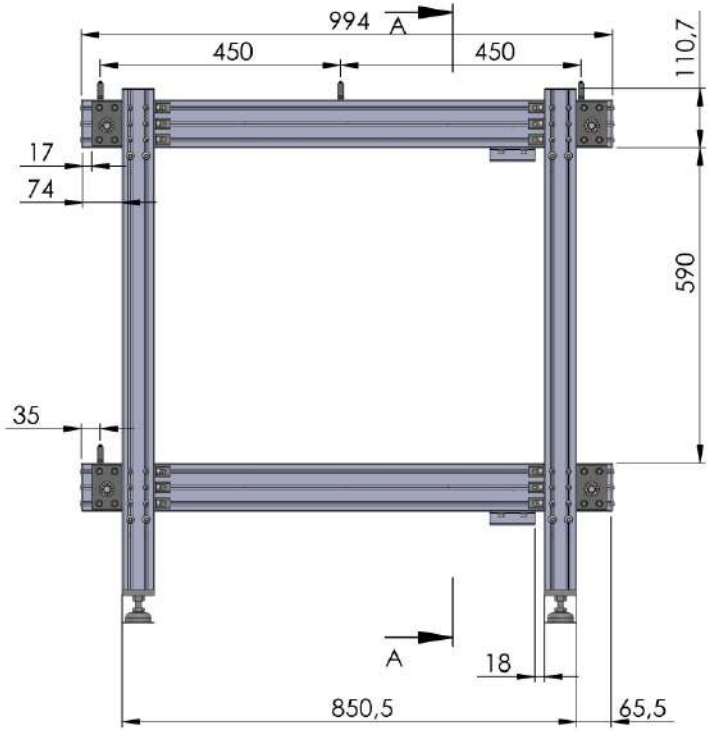


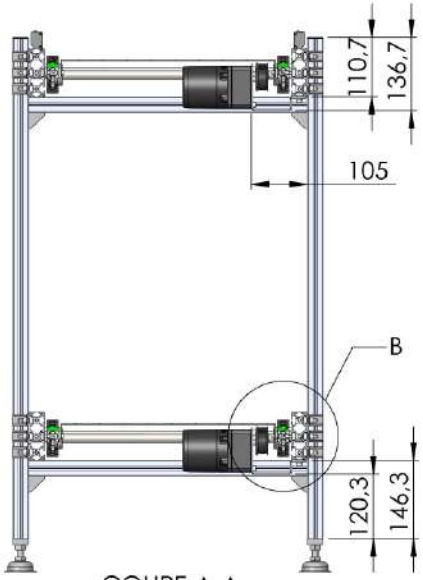

COUPE A-A
ECHELLE 1 : 10



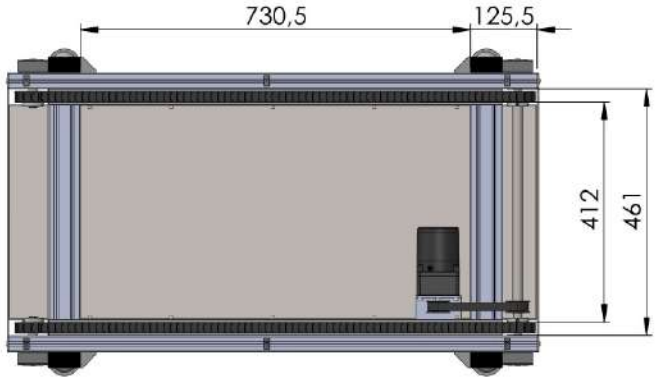

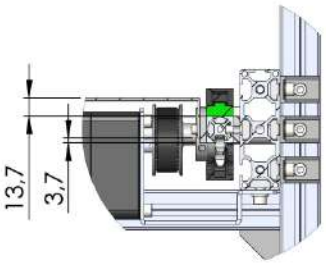

DÉTAIL B
ECHELLE 1 : 4

Ecole Nationale d'Ingénieurs de Bizerte			
Echelle : 1:10	**Convoyeur à deux étages**		Document 1
			Dessiné par: Hamdi.A
A3	© Ahmed Hamdi	Société: [redacted]	Page 2/2